

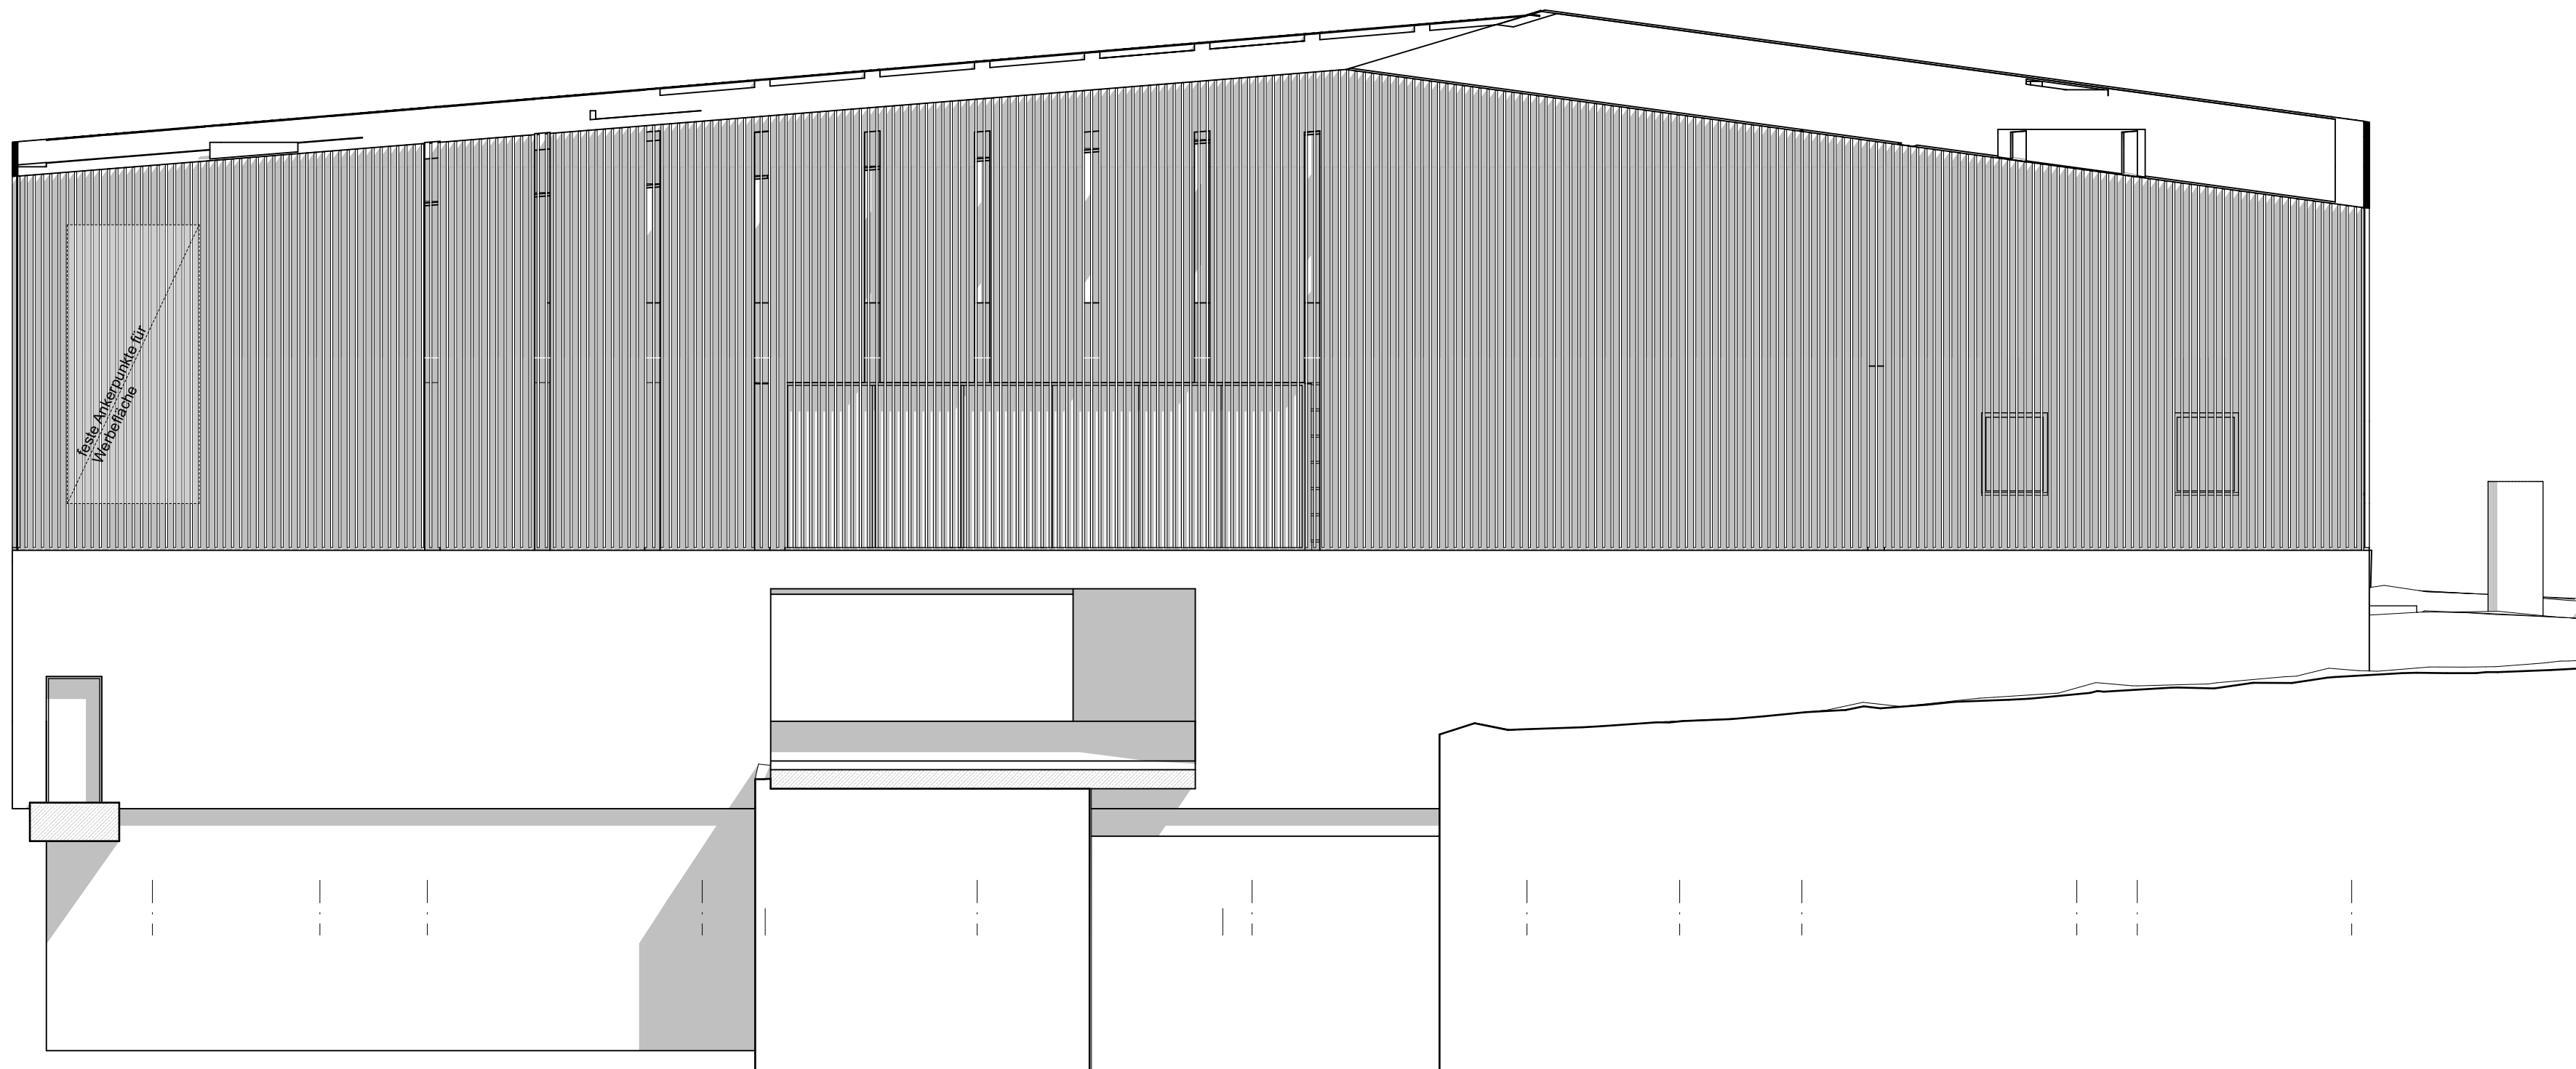


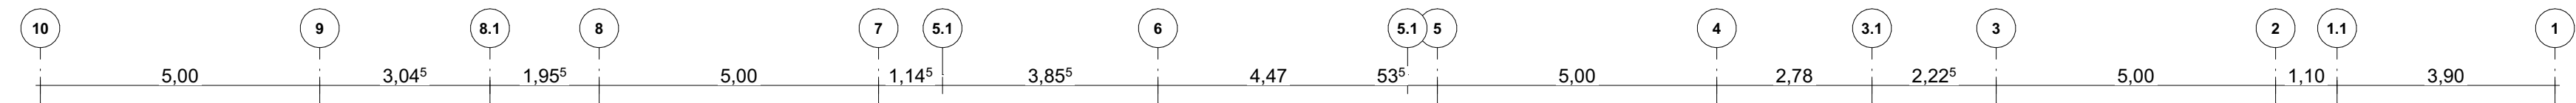


+617,30
OG

+613,80
EG

+610,69
UG

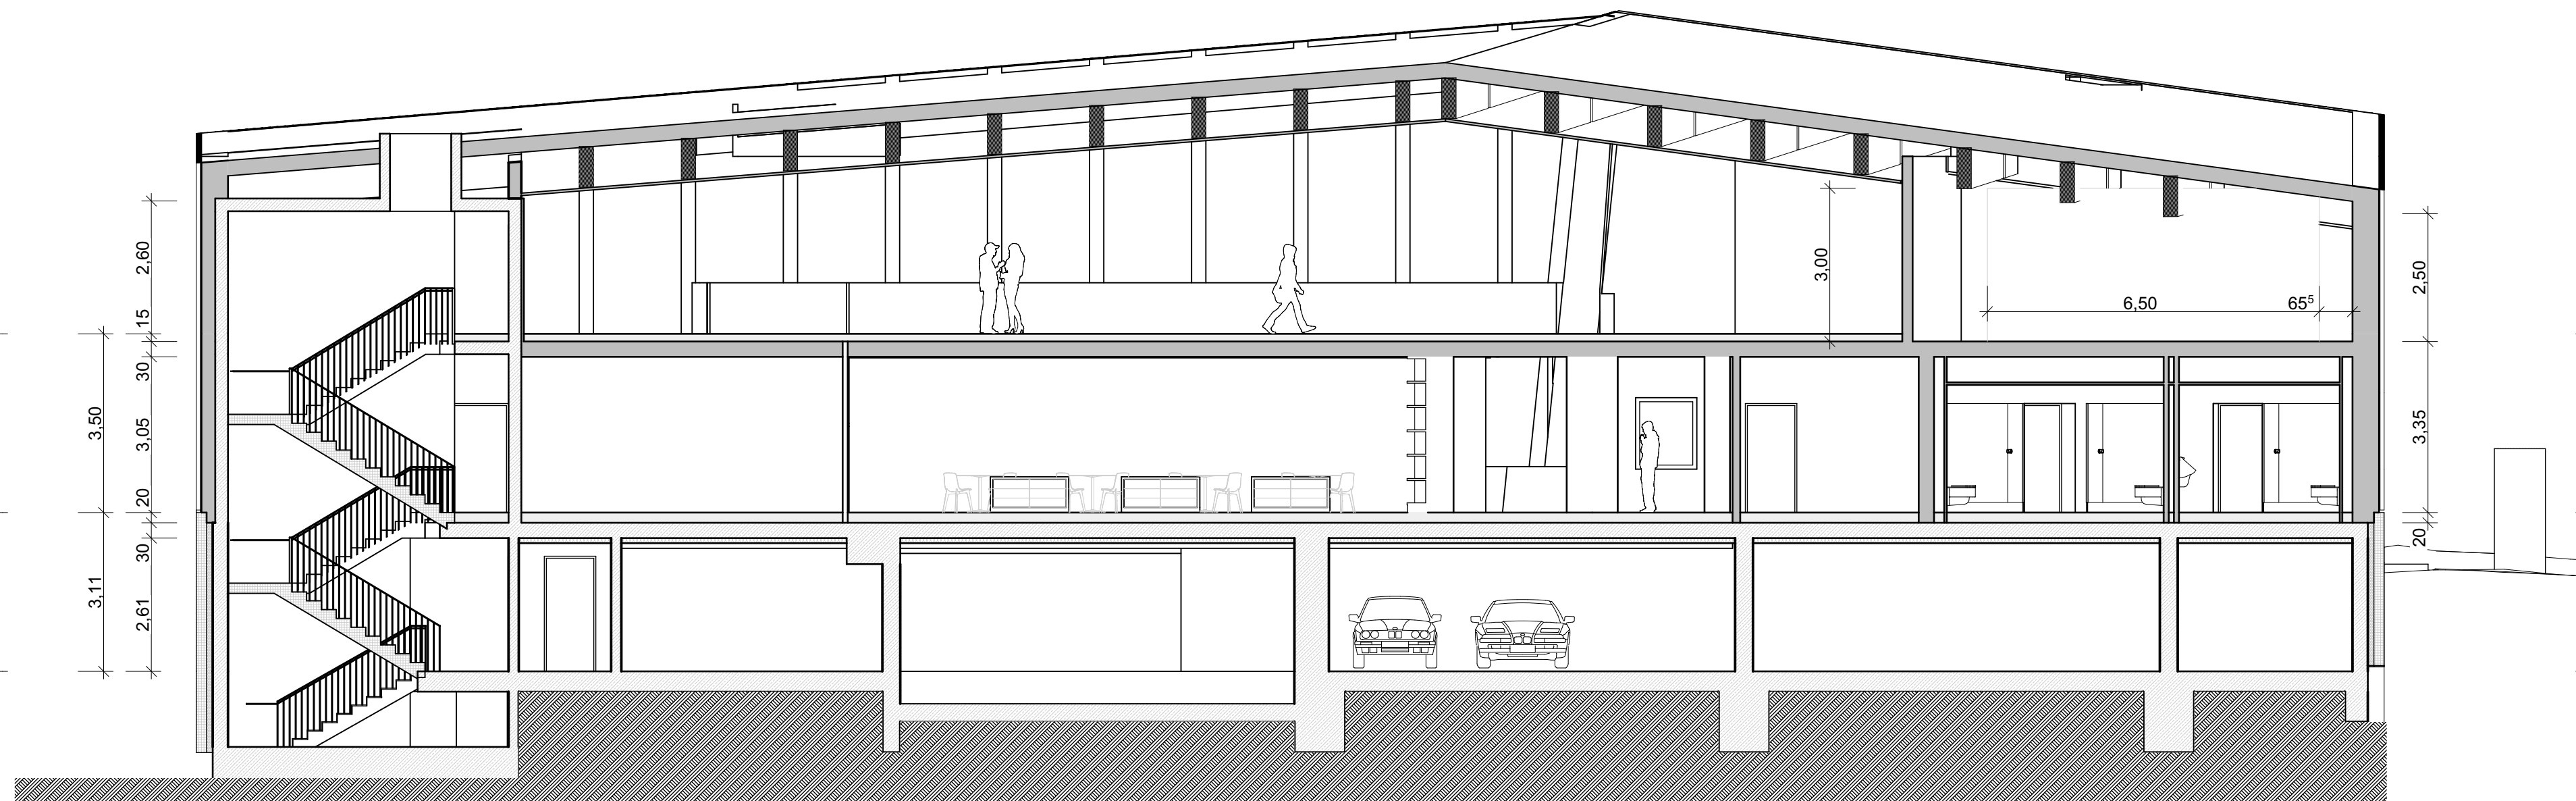

**Rathaus Bernried 3. Bauabschnitt:
Forum Humor**
Dorfstraße 26 Flur-Nr. XXX
D-82347 Bernried

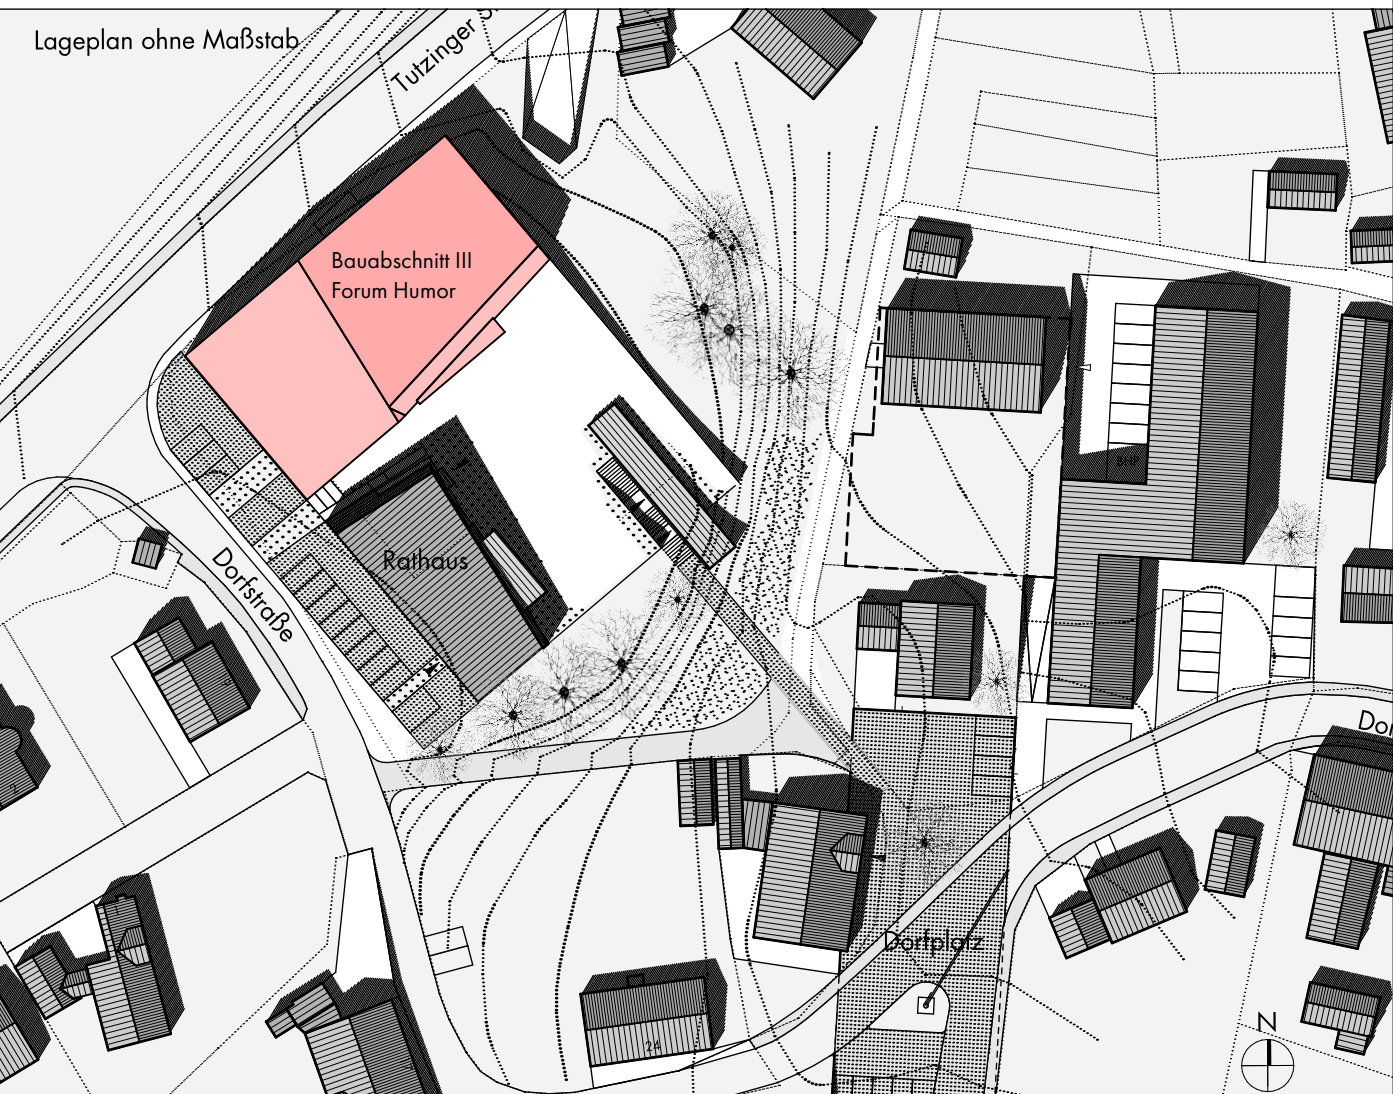

BAUHERR:	ARCHITEKT:
Gemeinde Bernried Dorfstraße 26 D-82347 Bernried T: 0821 599 605-0 M: gemeinde@bernried.de	Titus Bernhard Architekten Provinstraße 52, Gebäude B2 D-86153 Augsburg T: 0821 599 605-0 F: 0821 599 605-10 M: info@bernhardarchitekten.com

Status		ARBEITSSTAND	
Planinhalt		Plannummer	
Ansicht NW/ Schnitt I		ARC 2401 3	AN_NW_003
Maßstab		Planverf. Projekt LPH	Inhalt Blatt Nr. Index
1:100		Datum letzte Änderung	
Planformat		Erstellt	
		06.08.2026	