

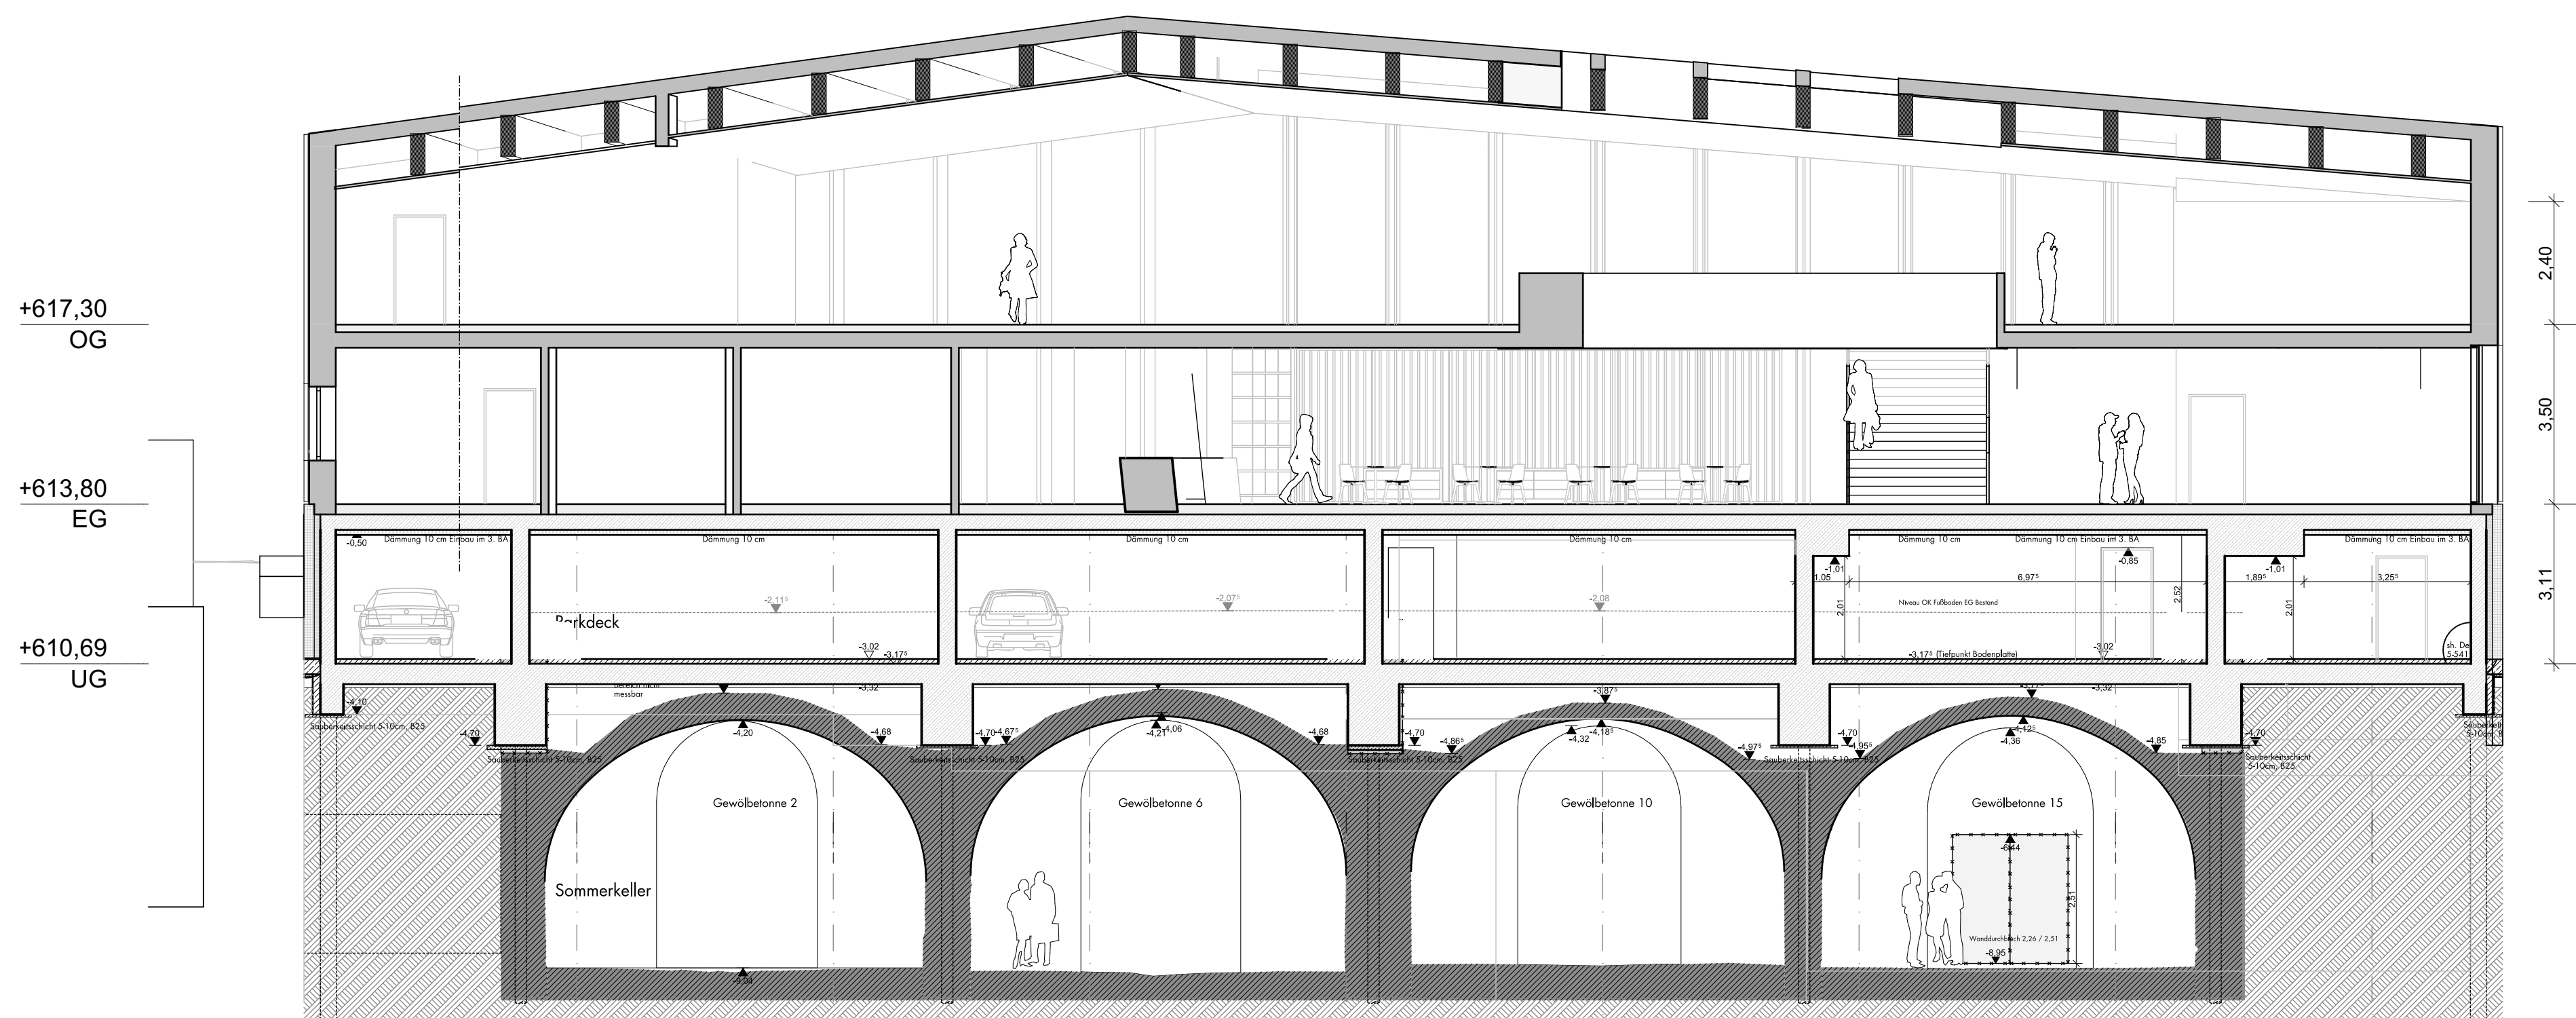


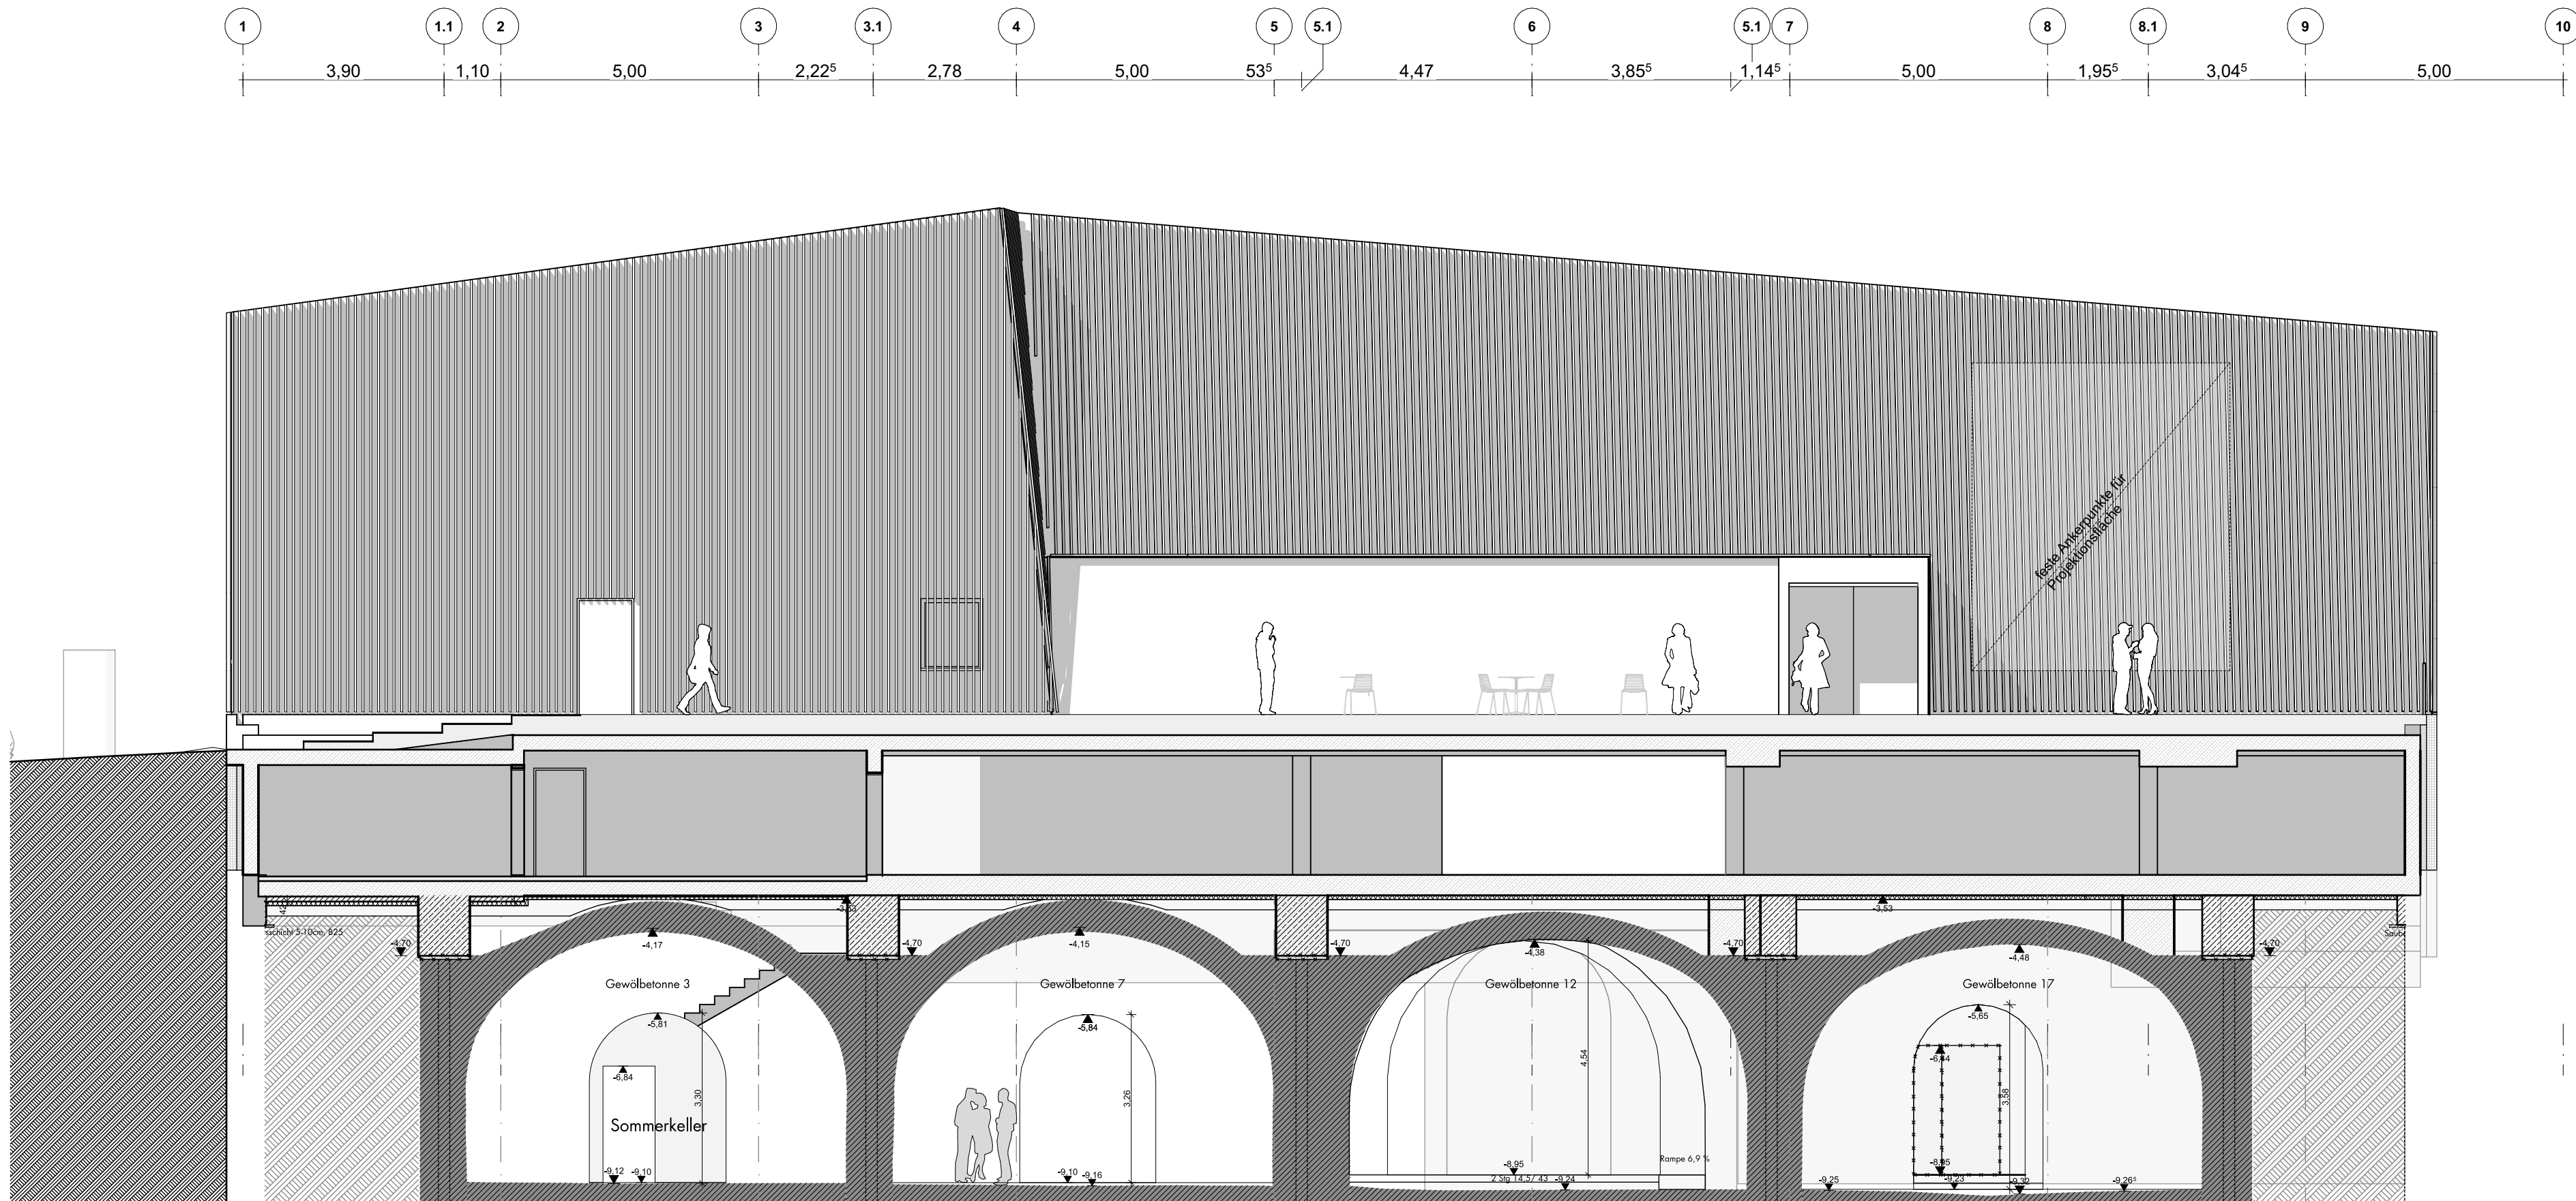

Rathaus Bernried 3. Bauabschnitt:
Forum Humor
Dorfstraße 26 Flur-Nr. XXX
D-82347 Bernried

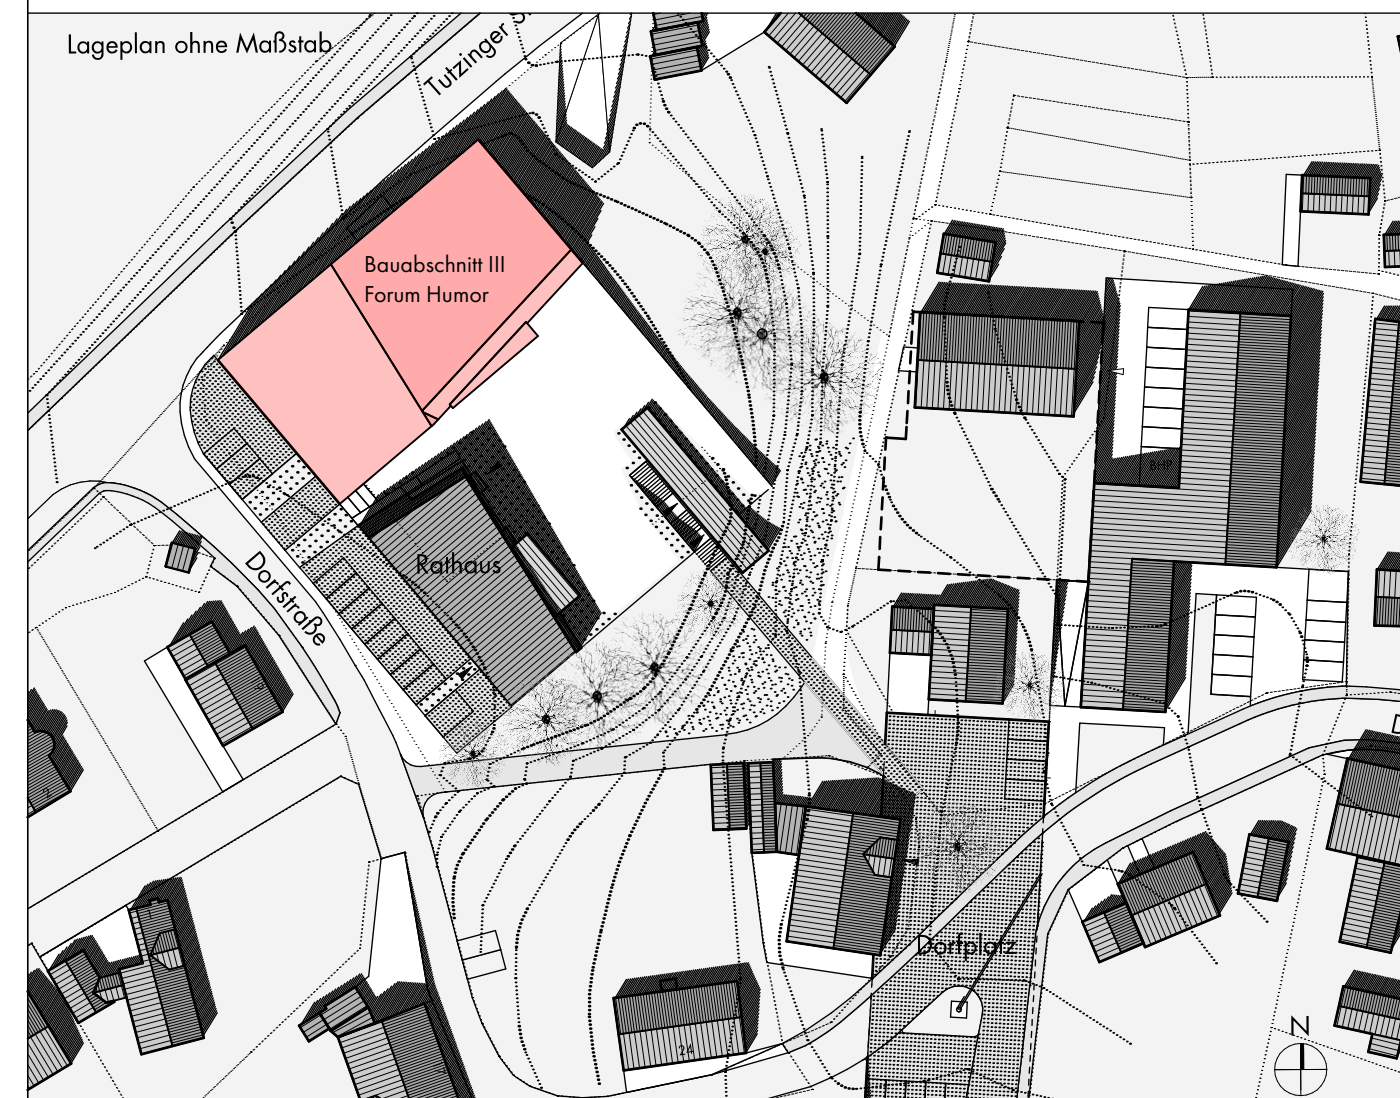

BAUHERR:
Gemeinde Bernried
Dorfstraße 26
D-82347 Bernried
T: 0821 599 605-0
M: gemeinde@bernried.de

ARCHITEKT:
Titus Bernhard Architekten
Provinstraße 52, Gebäude B2
D-86153 Augsburg
T: 0821 599 605-0
F: 0821 599 605-10
M: info@bernhardarchitekten.com

Planinhalt		Status	
Ansicht SO/ Schnitt F		ARBEITSSTAND	
Plannummer		2401 3	
Planverf.		Projekt LPH	
Maßstab		1:100	
Datum letzte Änderung		05.08.2024	