

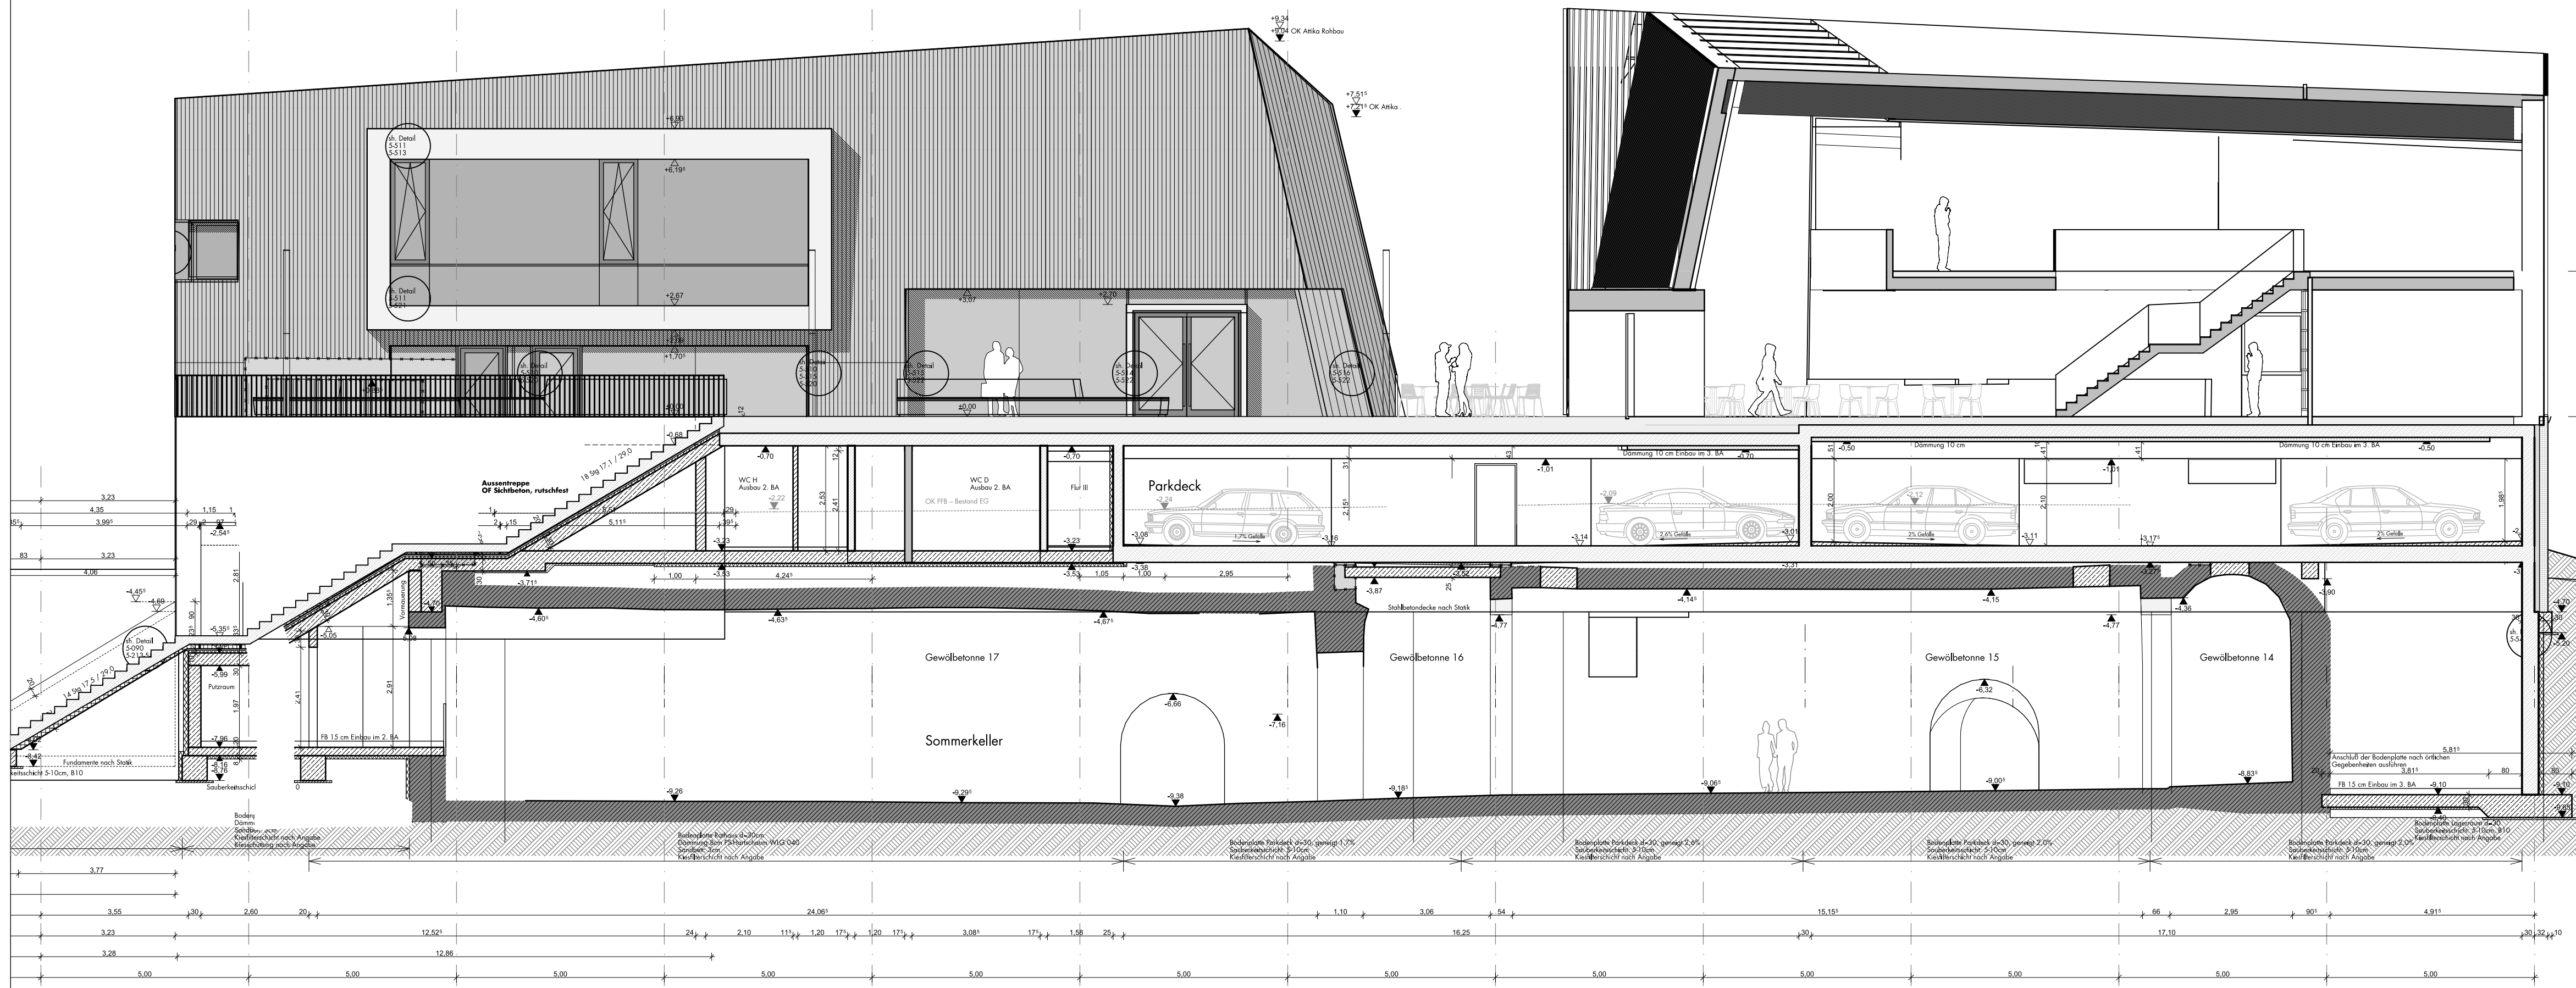


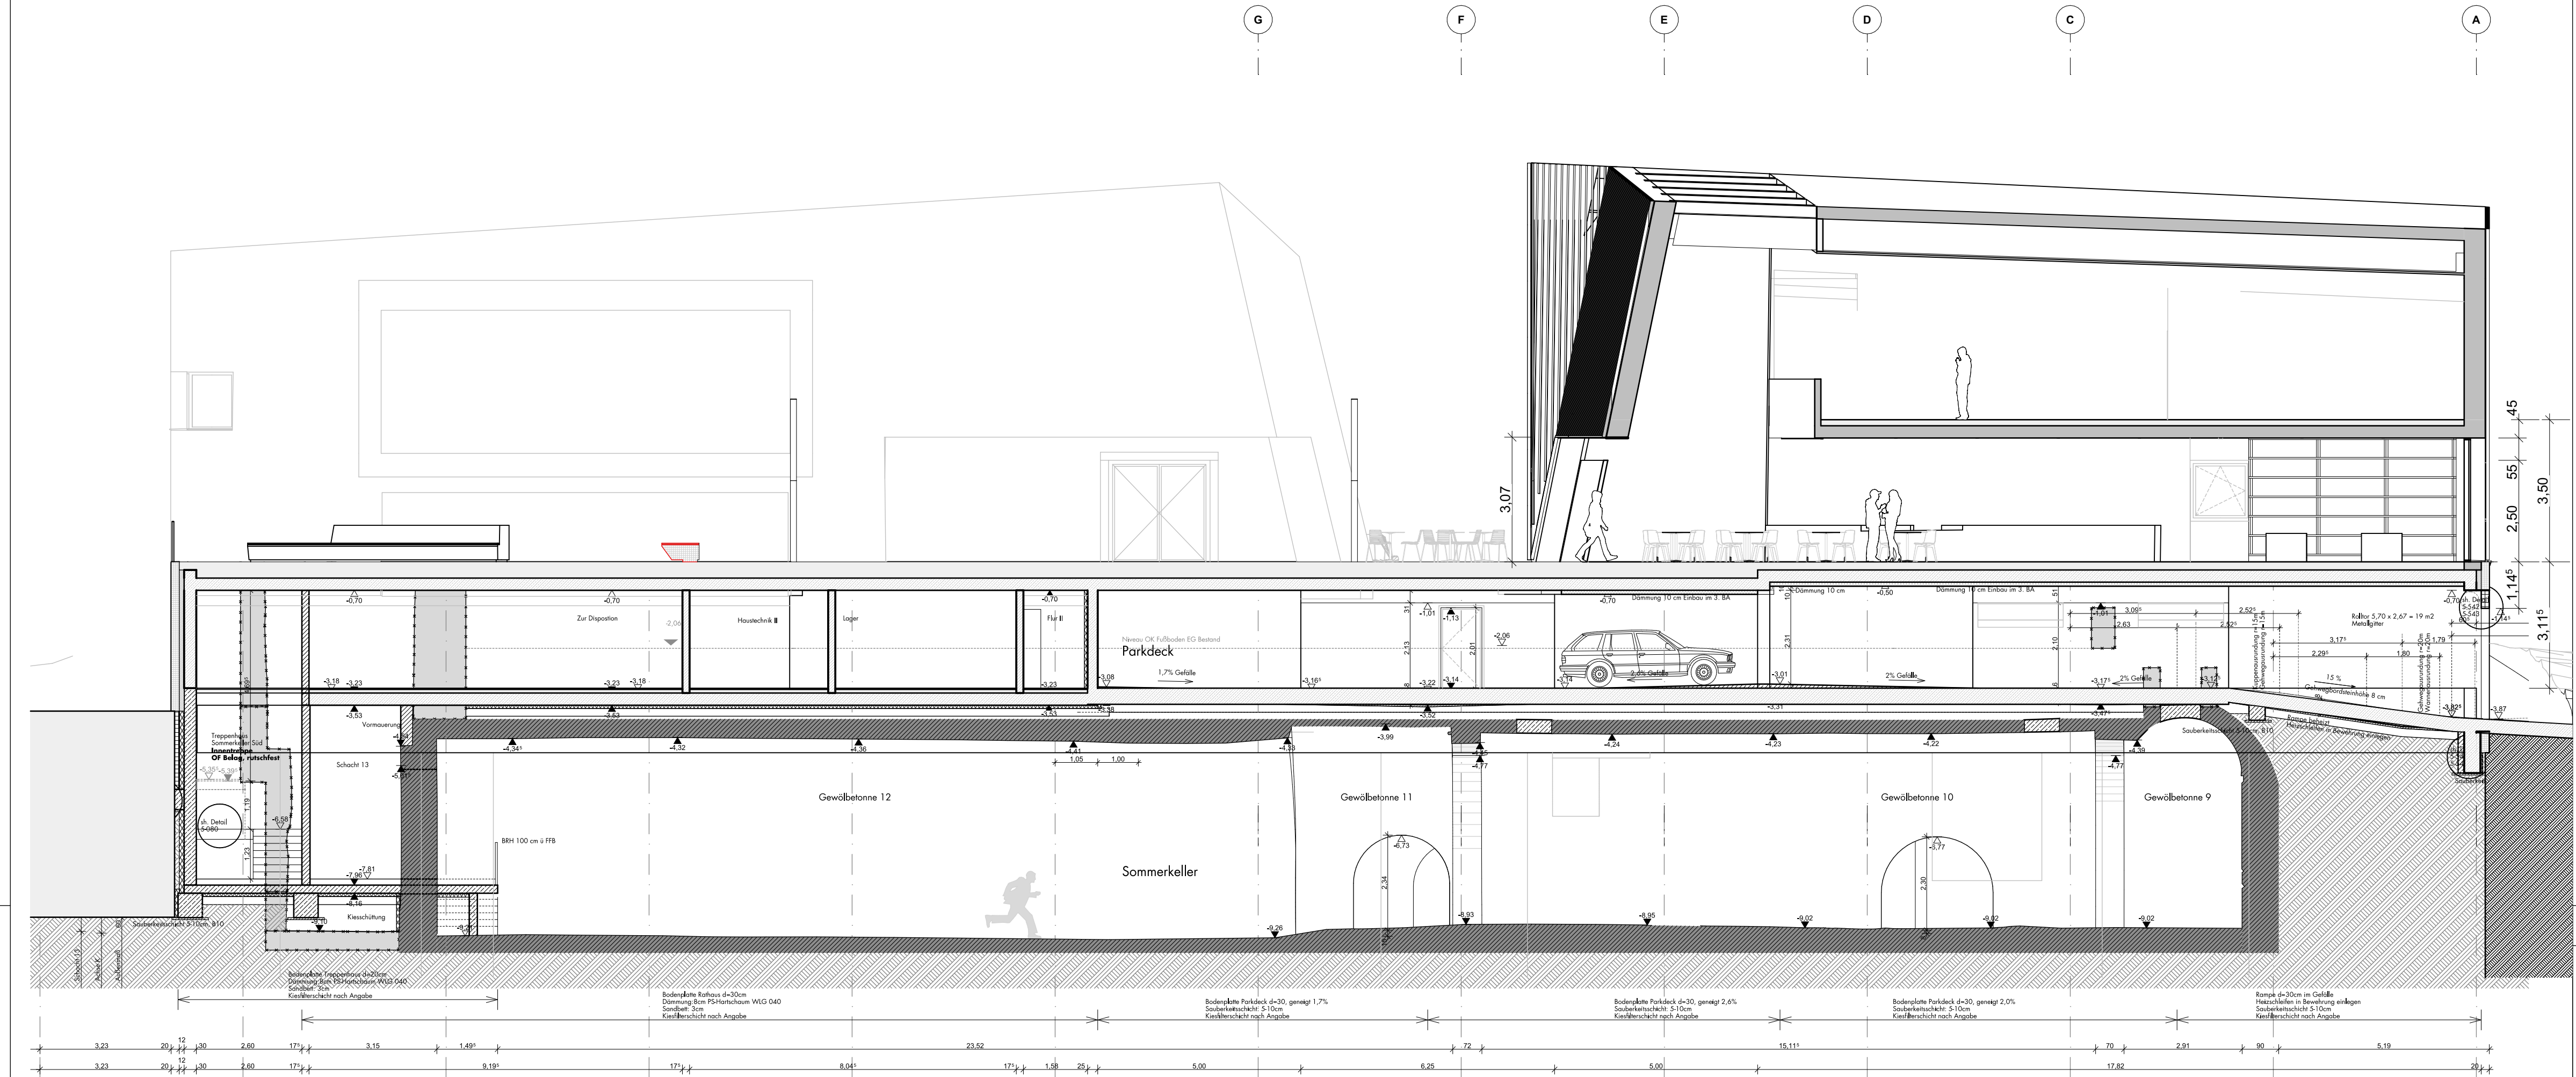

Rathaus Bernried 3. Bauabschnitt:
Forum Humor
Dorfstraße 26 Flur-Nr. XXX
D-82347 Bernried

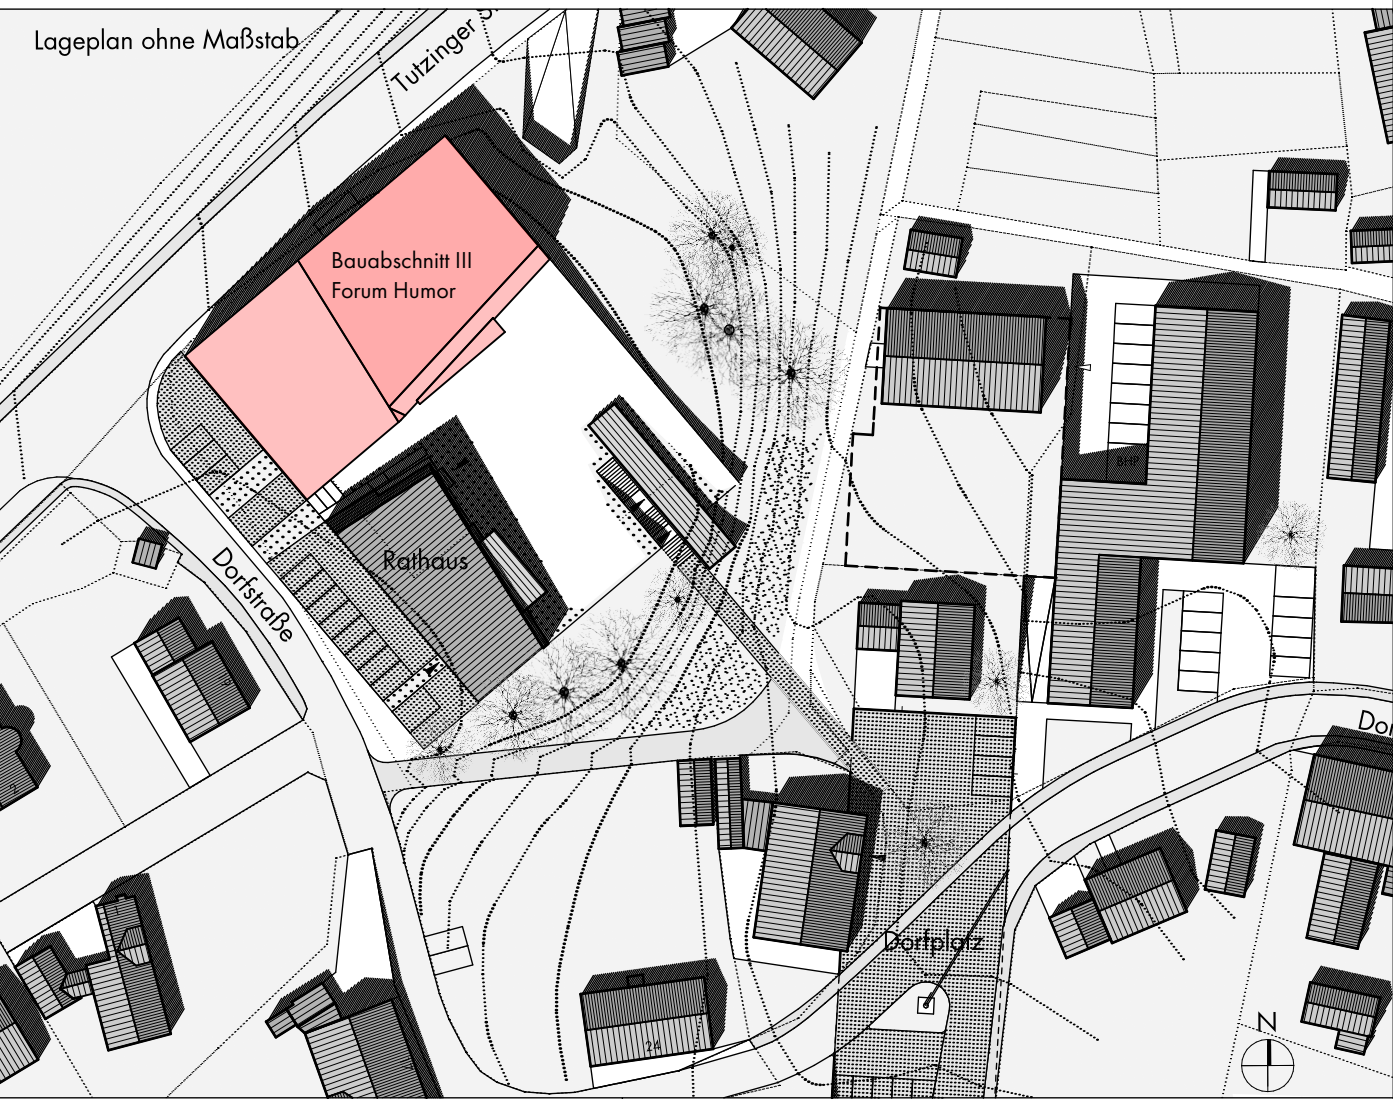

BAUHERR:		ARCHITEKT:	
Gemeinde Bernried Dorfstraße 26 D-82347 Bernried T: 0821 599 605-0 M: gemeinde@bernried.de		Titus Bernhard Architekten Provinzstraße 52, Gebäude B2 D-86153 Augsburg T: 0821 599 605-0 F: 0821 599 605-10 M: info@bernhardarchitekten.com	
Planinhalt		Status	
Schnitt C/ D		ARBEITSSTAND	
Maßstab		Datum letzte Änderung	
1:100			
Planformat		Erstellt	
		24.04.2024	